


LEGENDA DA FIAÇÃO

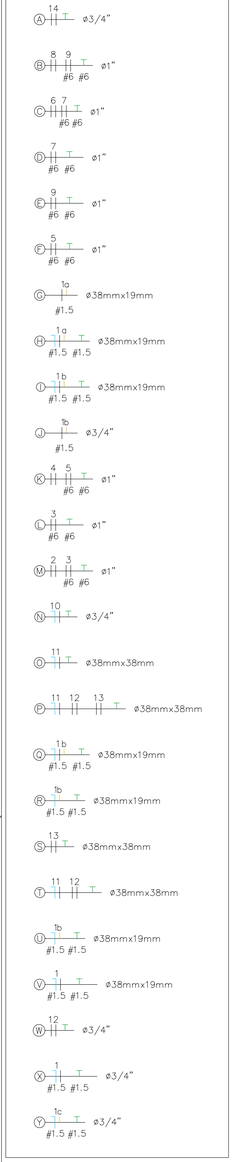

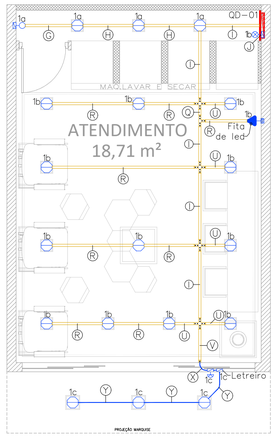


PLANTA LAYOUT
ESCALA 1:50

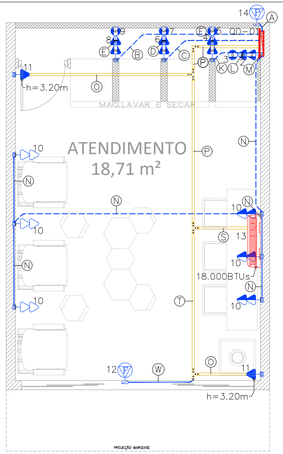



PLANTA LAYOUT
ESCALA 1:50

LEGENDA:

	– CAIXA 4X2" EMBUTIDO EM ALVENARIA
	– PONTO DE ILUMINAÇÃO
	– CONJUNTO 01 INTERRUPTOR SIMPLES EM CAIXA 4X2"
	– SENSOR FOTOCÉLULA
	– TIMER PARA ILUMINAÇÃO
	– CONJUNTO 02 TOMADAS 127V 10A BAIXA H=0.3M
	– CONJUNTO 02 TOMADAS 127V 10A MÉDIA H=1.1M
	– CONJUNTO 02 TOMADAS 220V 20A MÉDIA H=0.8M
	– CONJUNTO TOMADA 127V 10A ALTA H=3.2M
	– CONJUNTO TOMADA INDUSTRIAL SOBREPOR 2P+T 220V 32A MÉDIA H=1.2M
	– PONTO DE FORÇA – SAIDA DE FIO
	– PONTO ELÉTRICO NÃO PLUGÁVEL PARA PRESSURIZADOR
	– AR CONDICIONADO TIPO SPLIT – POTÊNCIA INDICADA
	– JUNÇÃO 'L' 38X38MM
	– JUNÇÃO 'T' 38X19MM – ILUMINAÇÃO
	– JUNÇÃO 'T' 38X38MM
	– JUNÇÃO 'X' 38X19MM – ILUMINAÇÃO
	– SAIDA FINAL 3/4" 38X19MM – ILUMINAÇÃO
	– QUADRO DE DISTRIBUIÇÃO DE EMBUTIR
	– ELETRODUTO NO TETO
	– ELETRODUTO NO PISO
	– PERFILADO PERFURADO NO TETO CHAPA N° 16 3 METROS 38MMX19MM
	– PERFILADO PERFURADO NO TETO CHAPA N° 16 3 METROS 38MMX38MM
	– NEUTRO, FASE, RETORNO, TERRA

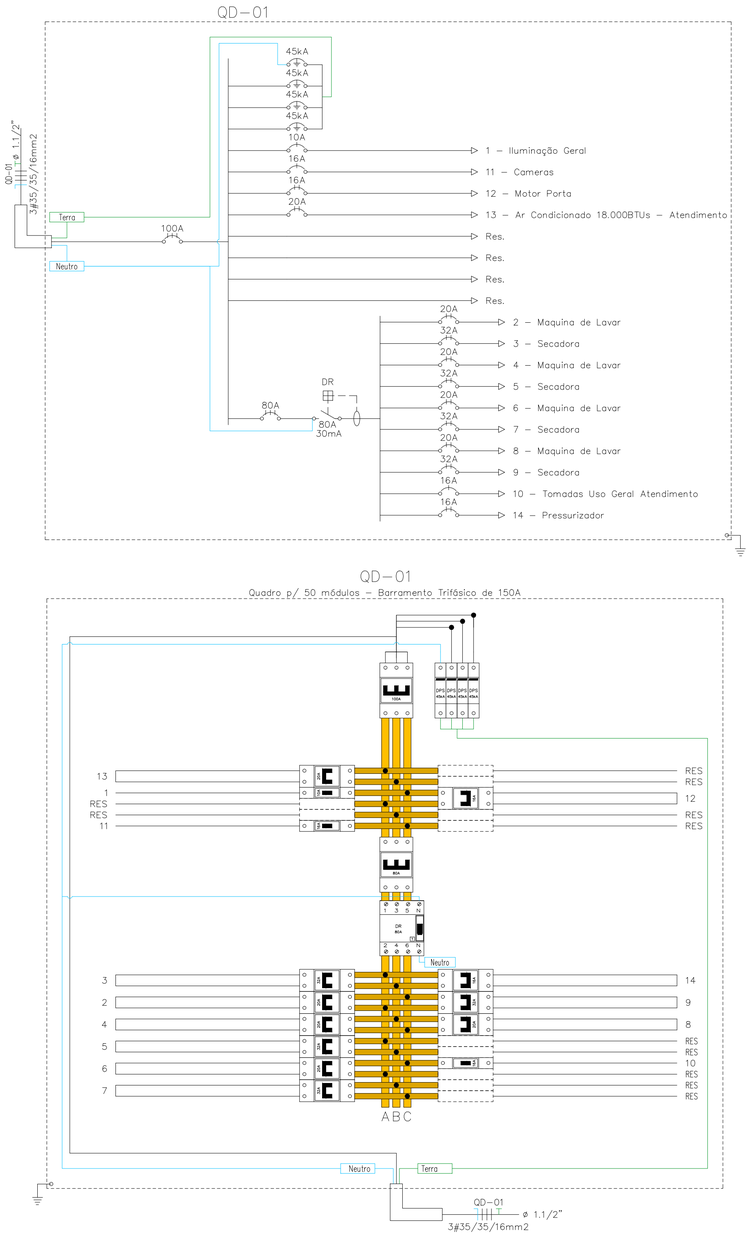

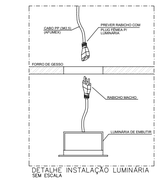

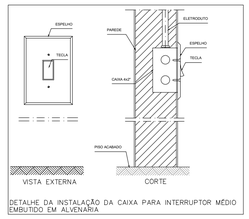







NOTAS IMPORTANTES:

1. PROJETO ELABORADO EM CONFORMIDADE COM A NBR5410 (INSTALAÇÕES ELÉTRICAS DE BAIXA TENSÃO);
2. O ENCAMINHAMENTO PODERÁ SER MODIFICADO CONFORME A NECESSIDADE EM CAMPO.
3. ENTRADA PADRÃO CPFL CATEGORIA C3 (DEMANDA ENTRE 30 E 38KVA): CAIXA III OU POLICARBONATO.
   - MEDIÇÃO DIRETA.
   - CABEAMENTO: #3x35mm²(F) + 35mm²(N) + 16mm²(T).
   - DISJUNTOR PROTEÇÃO: 100A.
   - ELETRODUTO: 1.1/2" (50mm).
   - ATERRAMENTO DO PADRÃO: CONDUTOR NU 10mm², ELETRODUTO 20mm.
4. OS ELETRODUTOS NÃO COTADOS NO PROJETO SERÃO DE 3/4".
5. OS CIRCUITOS DESTACADOS NA COR VERMELHA, DEVEM SER EXECUTADOS COM O DIMER, ANTES OU DEPOIS DOS INTERRUPTORES, CONFORME DETALHE 01.
6. TIPOS DE ELETRODUTO:
   - PAREDE: ELETRODUTO CORRUGADO COMUM LEVE, AMARELO;
   - LAJE/PISO: ELETRODUTO CORRUGADO REFORÇADO;
7. SUBTERRÂNEO: ELETRODUTO CORRUGADO REFORÇADO.
8. PREVER ARAME GUIA NOS ELETRODUTOS;
9. TODAS AS TUBULAÇÕES DE TELEFONE, DADOS, SOM E TV, SERÃO DE 1".
10. CONSIDERAR DUTOS DE CORES DIFERENTES PARA SISTEMAS.
11. ANTES DA CONCRETAGEM, PREVER DISPOSIÇÃO DAS TUBULAÇÕES E CAIXAS EMBUTIDAS EM RELAÇÃO AS ARMADURAS DOS PILARES, VIGAS E LAJES E AMARRAR AS TUBULAÇÕES NAS FERRAGENS UTILIZANDO AMARRIL.
12. ALTURA INDICADA EM PLANTA QUE NÃO FOR POSSÍVEL EXECUTAR DEVERÁ SER ADAPTADA.
13. CONFIRMAR ALTURA DE BALCÕES, BANCADAS, LAVATÓRIOS E OUTROS, ANTES DA INSTALAÇÃO DAS CAIXAS DE PASSAGEM, PARA EVITAR FUTUROS RETRABALHOS.
14. PREVER PÓ DE SERRA OU MATERIAL DE VEDAÇÃO NAS CAIXAS DE PASSAGEM E BOCAS DE TUBULAÇÃO ANTES DA CONCRETAGEM.
15. TODOS OS ELETRODUTOS INSTALADOS NO PISO DEVERÃO SER ENVELOPADOS, GARANTINDO ASSIM SUA ESTANQUEIDADE
16. TODAS AS FIAÇÕES NÃO COTADAS SERÃO DE 2,5mm².
17. TODOS OS CONDUTORES DE ATERRAMENTO, DEVERÃO TER A MESMA SEÇÃO DO CIRCUITO AO QUAL PERTENCEM OU IGUAL AO MAIOR CIRCUITO QUE ESTIVER AGRUPADO.
18. TODA FIAÇÃO DO TIPO "RABICHO" PARA ALIMENTAÇÃO DAS LUMINÁRIAS, SERÃO DE CABO MULTIPOLAR 3x1,5mm².
19. AS DERIVAÇÕES ACIMA DE #4mm² DEVEM SER FEITAS ATRAVÉS DE CONECTORES PRENSADOS.
20. UTILIZAR CABOS TIPO PP PARA ALIMENTAÇÃO DE PONTOS EXTERNOS E/OU AO TEMPO.
21. NA MONTAGEM DO QUADRO DE DISJUNTORES, BALANCEAR DE ACORDO COM O FASEAMENTO DO QUADRO DE CARGAS.
22. NO CASO DE EMENDAS EM CABOS DE ENERGIA, AS MESMAS SERÃO ESTANHADAS E FEITA SOMENTE DENTRO DE CAIXAS DE PASSAGEM E NUNCA NO INTERIOR DE ELETRODUTOS.
23. RESPEITAR O PADRÃO DE CORES PARA OS CABOS:
   - FASE = PRETO
   - NEUTRO = AZUL
   - TERRA = VERDE
   - RETORNO = BRANCO
24. ESPECIFICAÇÕES DOS CABOS:
   - CIRCUITOS DE DISTRIBUIÇÃO: ISOLAÇÃO 750V, 70°C TIPO AFUMEX OU SINTENAX;
   - CIRCUITOS ALIMENTADORES: ISOLAÇÃO 0,6/1KV 90°C TIPO EPROTENAX OU AFUMEX;
25. TOMADAS 220V SERÃO NA COR VERMELHA.
26. IDENTIFICAR OS DISJUNTORES NO QUADRO DE DISTRIBUIÇÃO
27. LUMINÁRIAS EXPOSTAS AO TEMPO SERÃO COM PROTEÇÃO IP65.
28. TODAS AS PARTES METÁLICAS NÃO CONDUTORAS TAIS COMO ELETROCALHAS, PERFILADOS, LUMINÁRIAS ETC, DEVERÃO SER ATERRADAS.
29. PONTOS DE ILUMINAÇÃO, TOMADAS DEVEM SEGUIR ALTURAS E COTAS DO PROJETO LUMINOTÉCNICO DISPONIVEL PELA ARQUITETURA.
30. A LISTA DE MATERIAIS ANEXADA A ESTE PROJETO TEM CARÁTER MERAMENTE INFORMATIVO, FUNCIONANDO COMO UMA SUGESTÃO PRELIMINAR DOS ITENS NECESSÁRIOS À EXECUÇÃO DA OBRA. A RESPONSABILIDADE PELA ESCOLHA, AQUISIÇÃO E ADEQUAÇÃO DOS MATERIAIS ESPECIFICADOS É EXCLUSIVAMENTE DO RESPONSÁVEL PELA OBRA OU EXECUÇÃO, QUE DEVERÁ VERIFICAR A CONFORMIDADE E A ADEQUAÇÃO DOS MESMOS ÀS NORMAS E ESPECIFICAÇÕES TÉCNICAS VIGENTES. NÃO NOS RESPONSABILIZAMOS POR QUAISQUER ERROS, OMISSÕES OU ALTERAÇÕES NOS ITENS DA LISTA.


OBSERVAÇÕES GERAIS


- Deve ser fixado no quadro de distribuição em lugar visível a seguinte advertência:


ADVERTÊNCIA

1. Quando um disjuntor atuar, desligando algum circuito ou a instalação inteira, a causa pode ser um sobrecarga ou um curto-circuito. Desligamentos frequentes são sinais de sobrecarga. Por isso, NUNCA troque os disjuntores por outros de maior capacidade (amperagem), simplesmente. Como regra, a troca de um disjuntor por outro de maior capacidade requer, antes, um redimensionamento do circuito através da troca de fios e cabos por outros de maior seção (bitola).


2. Da mesma forma, NUNCA desative ou remova a chave automática de proteção contra choques elétricos (Dispositivo DR), mesmo em caso de desligamentos sem causa aparente. Se os desligamentos forem frequentes e, principalmente, se as tentativas de religar a chave não tiverem êxito, isso significa, muito provavelmente, que a instalação elétrica apresenta anomalias internas, que só podem ser identificadas e corrigidas por profissionais qualificados.
A DESATIVAÇÃO OU REMOÇÃO DA CHAVE SIGNIFICA A ELIMINAÇÃO DE MEDIDA PROTETORA CONTRA CHOQUES ELÉTRICOS, ALÉM DE RISCO DE VIDA DOS USUÁRIOS DA INSTALAÇÃO.

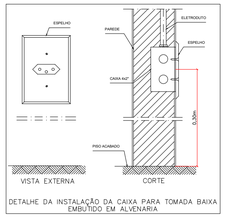

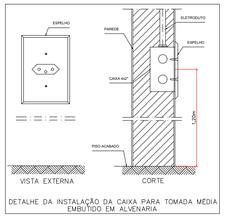


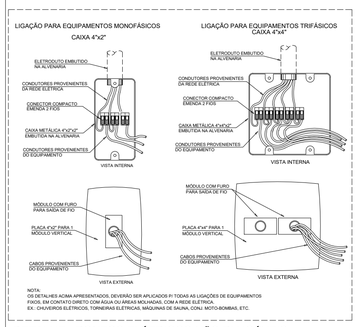

DETALHE - PONTOS ELÉTRICOS NÃO PLUGÁVEIS
SEM ESCALA

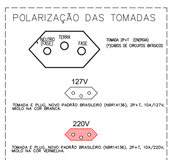

DETALHE - TOMADAS NBR
SEM ESCALA

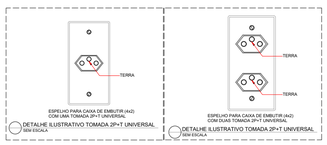

Quadro de Cargas

QD-01

Circ.	Descrição	Iluminação				Tomadas				Ar Cond.	Motores		Pot. W	Pot. V.A	Demanda (%)	Fat. Pot.	Corr. A	Fases	Prot. A	Cond. mm2	Fases ABC	Tipo de Cabo	Tensão V	Fase A	Fase B	Fase C
		10W	20W	30W	50W	100W	200W	2156W	4000W	1630W	200W	2CV														
1	Iluminação Geral	1	17	1	1								430.0	452.6	75%	0.95	2.67	1	10A	1,5	C	Fio cabo 750 V – PVC	127	0.0	0.0	452.6
2	Maquina de Lavar							1					2156.0	2269.5	100%	0.95	10.32	2	20A	2,5	CA	Fio cabo 750 V – PVC	220	1134.7	0.0	1134.7
3	Secadora								1				4000.0	4210.5	100%	0.95	19.14	2	32A	6	AB	Fio cabo 750 V – PVC	220	2105.3	2105.3	0.0
4	Maquina de Lavar							1					2156.0	2269.5	100%	0.95	10.32	2	20A	2,5	BC	Fio cabo 750 V – PVC	220	0.0	1134.7	1134.7
5	Secadora								1				4000.0	4210.5	100%	0.95	19.14	2	32A	6	AB	Fio cabo 750 V – PVC	220	2105.3	2105.3	0.0
6	Maquina de Lavar							1					2156.0	2269.5	100%	0.95	10.32	2	20A	2,5	CA	Fio cabo 750 V – PVC	220	1134.7	0.0	1134.7
7	Secadora								1				4000.0	4210.5	100%	0.95	19.14	2	32A	6	BC	Fio cabo 750 V – PVC	220	0.0	2105.3	2105.3
8	Maquina de Lavar							1					2156.0	2269.5	100%	0.95	10.32	2	20A	2,5	BC	Fio cabo 750 V – PVC	220	0.0	1134.7	1134.7
9	Secadora								1				4000.0	4210.5	100%	0.95	19.14	2	32A	6	CA	Fio cabo 750 V – PVC	220	2105.3	0.0	2105.3
10	Tomadas Uso Geral Atendimento						6						1200.0	1263.2	75%	0.95	7.46	1	16A	2,5	C	Fio cabo 750 V – PVC	127	0.0	0.0	1263.2
11	Cameras					2							200.0	210.5	75%	0.95	1.24	1	16A	2,5	C	Fio cabo 750 V – PVC	127	0.0	0.0	210.5
12	Motor Porta											1	200.0	210.5	90%	0.95	0.96	2	16A	2,5	CA	Fio cabo 750 V – PVC	220	105.3	0.0	105.3
13	Ar Condicionado 18.000BTUs – Atendimento									1			1630.0	1715.8	100%	0.95	7.80	2	20A	2,5	AB	Fio cabo 750 V – PVC	220	857.9	857.9	0.0
14	Pressurizador											1	1471.0	1548.4	100%	0.95	7.04	2	16A	2,5	AB	Fio cabo 750 V – PVC	220	774.2	774.2	0.0
RES.	Circuito Reserva																									
RES.	Circuito Reserva																									
RES.	Circuito Reserva																									
RES.	Circuito Reserva																									
Total		1	17	1	1	2	6	4	4	1	1	1	29755.0	31321.1									10322.7	10217.4	10781.0
Aliment.	C=15.88m QT=2%												29277.5	30818.4	100%	0.95	81.10	3	100A	35	ABC	Cabo 1 KV – EPR	220	10322.7	10217.4	10781.0

Potência Total (29755.0 W) (31321.1 V.A) Potência Demandada: 98.4% (29277.5 W) (30818.4 V.A)

Corrente nas Fases: A=93.8A B=92.9A C=91.8A

R00	EMISSÃO	25/03/2026
REVISÃO	DESCRIÇÃO	DATA

CLIENTE :
KARINA MACHADA GAMA

OBRA:
SALA COMERCIAL
AV. ENG. NEWTON FLAVIO SILVA PINTO, 0002645 - SALA 04
PARQUE RESIDENCIAL CELINA DALUL - MIRASSOL - SP

TÍTULO:
PROJETO DE INSTALAÇÕES ELÉTRICAS
PLANTAS ILUMINAÇÃO, TOMADAS E SISTEMAS

PROPRIETÁRIO:
KARINA MACHADA GAMA

RESPONSÁVEL TÉCNICO :
ENG. CIVIL JONATHAN PEREIRA ROSSATTO
CREA: 5069377611

REVISÃO: R00
TIPO: ELE
FOLHA: 01/01

RIOPRENGENGENHARIA
Endereço: Rua Treze de Maio, nº 130 - Vila Goyos
São José do Rio Preto/SP. - Tel.: (17) 3308-9890

- Projetos de Fundações;
- Projetos de Estrutura em Concreto Armado;
- Projetos de Estrutura Metálicas;
- Projetos de Instalações Hidrossanitários;
- Projetos de Instalações Elétricas;
- Projetos de Infraestrutura Urbana;
- Projetos de Sistemas Viários;
- Projeto de Prevenção e Combate a Incêndios.

PROJETO	FC
VERIFICADO	JPR
APROVADO	JPR

ART:
Nº DE PROJETO: 072_26

DIREITOS AUTORAIS RESERVADOS. PROIBIDA SUA REPRODUÇÃO TOTAL OU PARCIAL SEM PREVIA AUTORIZAÇÃO.

ISO FULL BLEED A1 (841.00 X 594.00 MM)