




PLANTA BAIXA: TÉRREO (ESGOTO)
ESCALA: 1:25

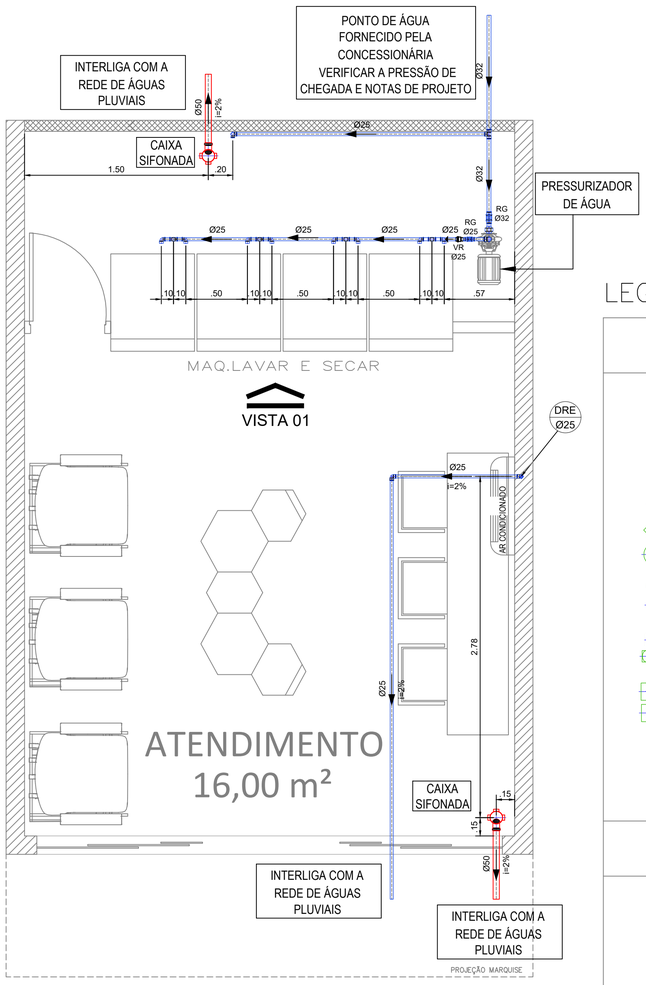

PLANTA BAIXA: TÉRREO (ÁGUA)
ESCALA: 1:25

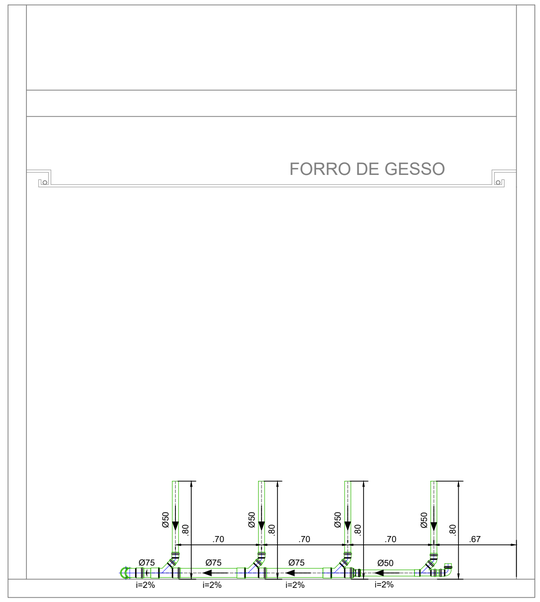

VISTA 01 - ESPUMA
ESC. 1:25

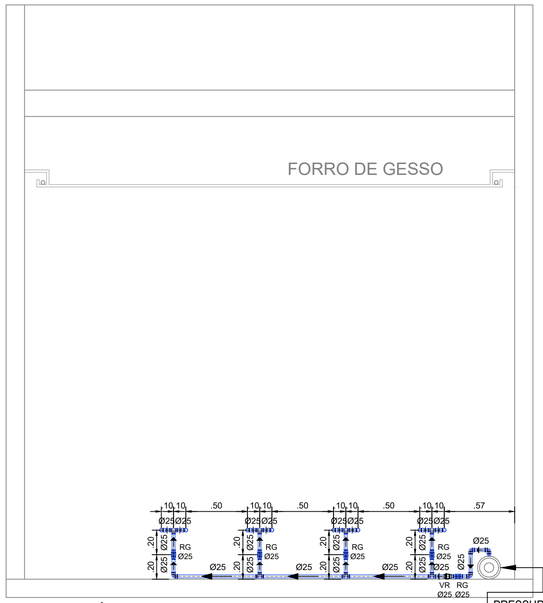

VISTA 01 - ÁGUA FRIA
ESC. 1:25

NOTAS GERAIS

- AS COTAS SÃO CONSIDERADAS DE PISO E PAREDE ACABADOS, DEVERÃO SER CHECADAS NA OBRA.
- NENHUMA TUBULAÇÃO EMBUTIDA NO CONTRAPISO OU ALVENARIA PODERÁ SER FECHADA SEM O TESTE DE ESTANQUEIDADE E A LIBERAÇÃO FEITA PELA FISCALIZAÇÃO
- AS TUBULAÇÕES DE ÁGUA FRIA SERÃO EM PVC SOLDÁVEL MARROM COM SAÍDAS PARA AS PEÇAS SANITÁRIAS COM CONEXÕES MISTAS (AZUL) COM BUCHA DE LATÃO.
- AS TUBULAÇÕES DE ESGOTO SANITÁRIO TERÃO DECLIVIDADE MÍNIMA DE 2% PARA TUBOS ATÉ Ø75mm E 1,0% PARA TUBOS DE Ø100mm.
- DEVERÁ CONFERIR AS MEDIDAS ANTES DA EXECUÇÃO DOS SERVIÇOS
- O PONTO DE ÁGUA FORNECIDO PELA CONCESSIONÁRIA COM REGISTRO DE GAVETA DE Ø1" COM ROSCA, A PRESSÃO DE ENTRADA DE ÁGUA DEVE TER NO MÍNIMO DE 1,5 BAR E MÁX. DE 8,2 BAR (ENTRE 15,3 E 84 m DE COLUNA D' ÁGUA) CASO A PRESSÃO SEJA INFERIOR A 1,5 BAR, DEVE SER COLOCADO O PRESSURIZADOR PARA AUMENTÁ-LA, ELE DEVE SER COLOCADO APÓS A SAIDA DE ÁGUA DO REGISTRO. SE A PRESSÃO FOR SUPERIOR A 8,2 BAR DEVE SER POSTO UM REGULADOR DE PRESSÃO PARA DIMINUI-LA.

LEGENDA:

PVC Soldável branco

- Cap 50mm (Detalhado/em Planta)
- Cap 50mm (Detalhado/Sobe)
- Joelho 45 50mm (Detalhado/em Planta)
- Joelho 45 50mm (Detalhado/Sobe)
- Joelho 45 75mm (Detalhado/Desce)
- Joelho 45 75mm (Detalhado/em Planta)
- Joelho 45 75mm (Detalhado/Lateral)
- Joelho 90 50mm (Detalhado/em Planta)
- Joelho 90 50mm (Detalhado/Frontal)
- Junção 50mm (Detalhado/em Planta)
- Junção 50mm (Detalhado/Frontal)
- Junção 75x50mm (Detalhado/em Planta)
- Junção 75x50mm (Detalhado/Frontal)
- Luva 50mm (Detalhado/em Planta)
- Luva 75mm (Detalhado/em Planta)
- Luva 75mm (Detalhado/Frontal)
- Redução excêntrica 75x50mm (Detalhado/em Planta)

PVC Soldável marrom

- Adaptador soldável curto bolsa e rosca 25mmx3/4" (Detalhado/em Planta)
- Adaptador soldável curto bolsa e rosca 32mmx1" (Detalhado/em Planta)
- Joelho 90 25mm (Detalhado/em Planta)
- Joelho 90 25mm (Detalhado/Sobe)
- Joelho 90 32mm (Detalhado/Desce)
- Joelho 90 com rosca 25mmx1/2" (Detalhado/Lateral)
- Joelho 90 com rosca 25mmx3/4" (Detalhado/em Planta)
- Joelho 90 com rosca 25mmx3/4" (Detalhado/Sobe)
- Tê 25mm (Detalhado/Desce)
- Tê 25mm (Detalhado/em Planta)
- Tê de redução 32x25mm (Detalhado/em Planta)
- União 32mm (Detalhado/em Planta)

Registros,Valv.,Hid

- Registro de Gaveta base 1" (Detalhado/em Planta)
- Registro de Gaveta base 3/4" (Detalhado/em Planta)

PVC Águas Pluviais

- Caixa Sifonada 100x100x50mm (Detalhado/em Planta)

PRUMADAS

DRE Ø25 – Dreno ar condicionado

TUBULAÇÃO

- PVC Águas Pluviais – Tubo PVC Aguas Pluviais 50mm (Detalhado)
- Tubo PVC Soldável branco 50mm (Detalhado)
- Tubo PVC Soldável branco 75mm (Detalhado)
- Tubo PVC Soldável marrom (NBR 5648/pe CP19) 25mm (Detalhado)
- Tubo PVC Soldável marrom (NBR 5648/pe CP19) 32mm (Detalhado)

PVC Soldável branco

Quant.	Und.	Dimensão	Descrição
1.17	m	75mm	Tubo PVC Soldável branco
2.83	m	50mm	Tubo PVC Soldável branco
1	pc	50mm	Cap
1	pc	75mm	Joelho 45
4	pc	50mm	Joelho 45
1	pc	50mm	Joelho 90
3	pc	75mmx50mm	Junção
1	pc	50mm	Junção
3	pc	75mm	Luva
1	pc	50mm	Luva
1	pc	75mmx50mm	Redução excêntrica

PVC Soldável marrom


Quant.	Und.	Dimensão	Descrição
1.57	m	32mm	Tubo PVC Soldável marrom (NBR 5648/pe CP19)
10.04	m	25mm	Tubo PVC Soldável marrom (NBR 5648/pe CP19)
2	pc	32mmx1"	Adaptador soldável curto bolsa e rosca
10	pc	25mmx3/4"	Adaptador soldável curto bolsa e rosca
7	pc	25mm	Joelho 90
1	pc	25mmx1/2"	Joelho 90 com rosca
8	pc	25mmx3/4"	Joelho 90 com rosca
7	pc	25mm	Tê
1	pc	32mmx25mm	Tê de redução
1	pc	32mm	União

Registros,Valv.,Hid

Quant.	Und.	Dimensão	Descrição
1	pc	1"	Registro de Gaveta base
5	pc	3/4"	Registro de Gaveta base

PVC Águas Pluviais

Quant.	Und.	Dimensão	Descrição
1.12	m	50mm	Tubo PVC Aguas Pluviais
2	pc	100x100x50mm	Caixa Sifonada

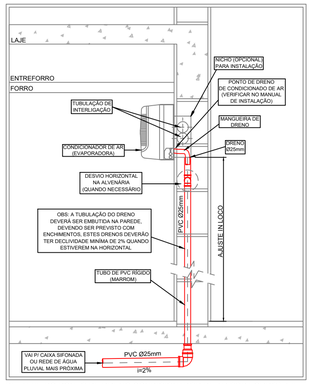

DETALHE DO PONTO DE DRENO CONDICIONADOR DE AR SOB FORRO/LAJE
Sem escala

R00	EMISSÃO	26/03/2026
REVISÃO	DESCRIÇÃO	DATA

CLIENTE : KARINA MACHADA GAMA

OBRA: SALA COMERCIAL
AV. ENG. NEWTON FLAVIO SILVA PINTO, 0002645 - SALA 04
PARQUE RESIDENCIAL CELINA DALUL - MIRASSOL - SP

TÍTULO: PROJETO DE INSTALAÇÕES HIDRÁULICAS

REVISÃO: R00

TIPO: HID

FOLHA: 01/01

PROPRIETÁRIO: KARINA MACHADA GAMA

RESPONSÁVEL TÉCNICO : ENG. CIVIL JONATHAN PEREIRA ROSSATTO
CREA: 5069377611

RIOPRENENGENHARIA
Endereço: Rua Treze de Maio, nº 130 - Vila Goyos
São José do Rio Preto/SP. - Tel.: (17) 3308-9890

- Projetos de Fundações;
- Projetos de Estrutura em Concreto Armado;
- Projetos de Estrutura Metálicas;
- Projetos de Instalações Hidrossanitários;
- Projetos de Instalações Elétricas;
- Projetos de Infraestrutura Urbana;
- Projetos de Sistemas Viários;
- Projeto de Prevenção e Combate a Incêndios.

PROJETO	JPR
VERIFICADO	JPR
APROVADO	JPR

ART: Nº DE PROJETO: 072_26

DIREITOS AUTORAIS RESERVADOS. PROIBIDA SUA REPRODUÇÃO TOTAL OU PARCIAL SEM PREVIA AUTORIZAÇÃO.

ISO A1 (841X594)mm